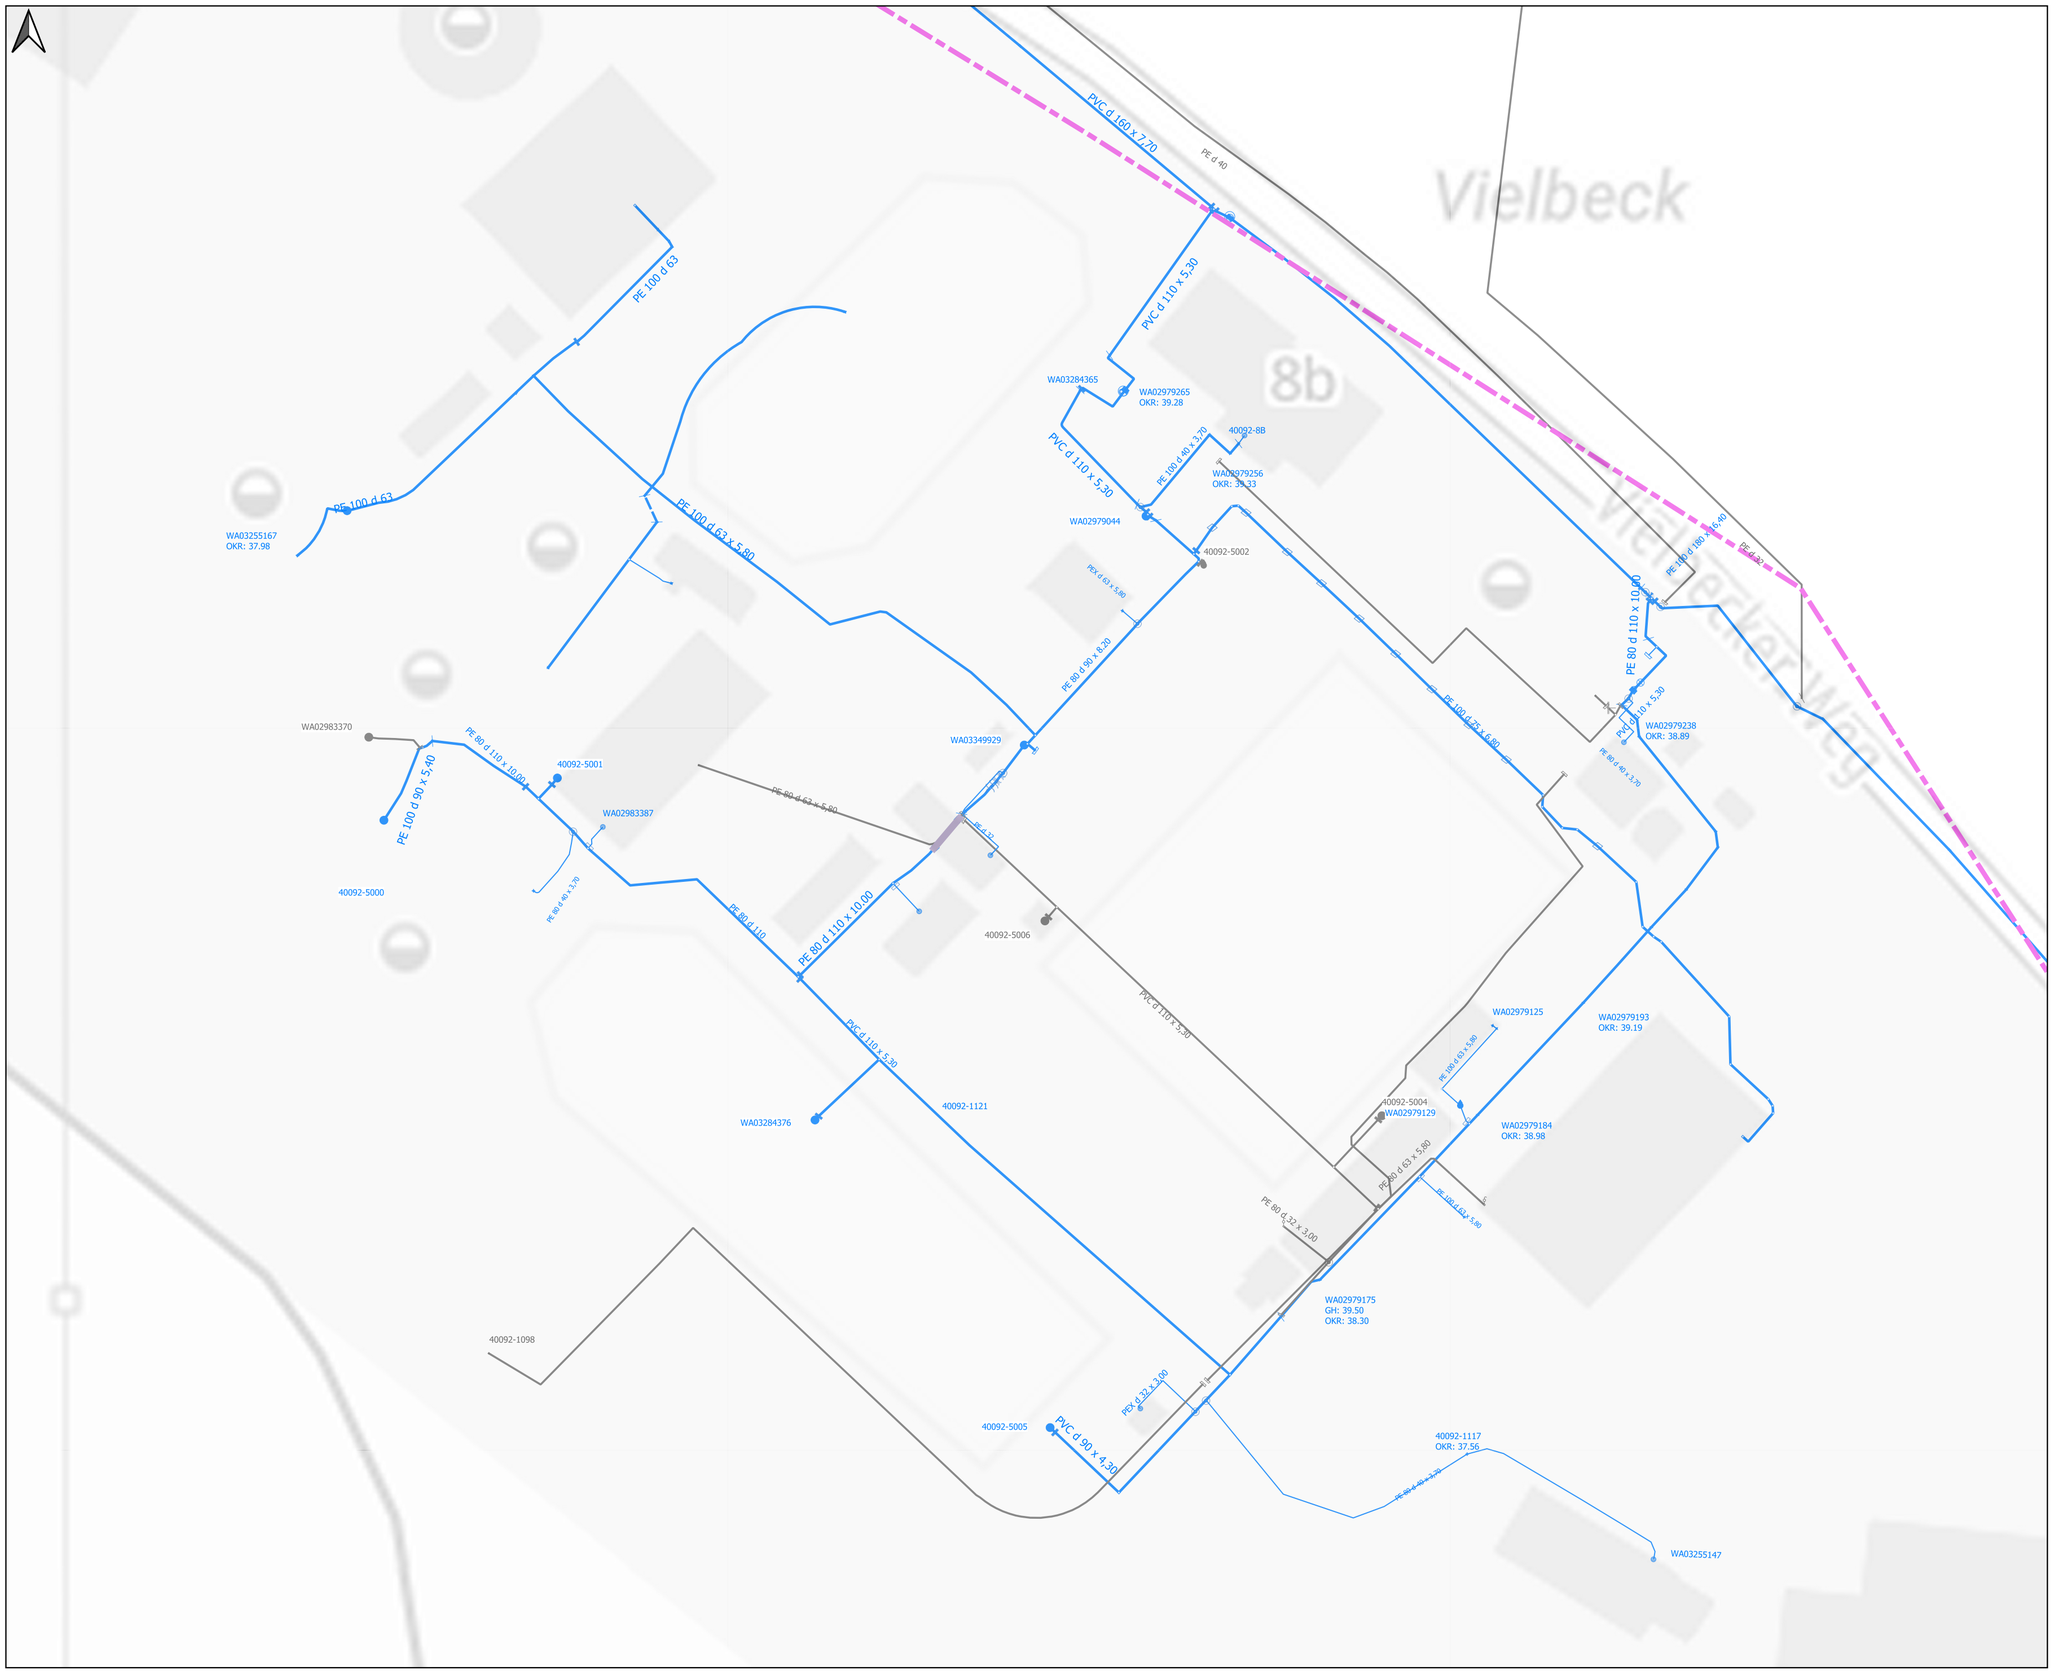

Legende

Darstellung Wasserversorgung

- Trinkwasserversorgungsleitung *E****Z.**BZ
- Trinkwasseranschlussleitung *E*Z_BZ
- Rohwasserleitung *E*Z_BZ
- Brauchwasserleitung *E*Z_BZ
- wasserleitung *E*****U_BU
- wasserleitung *E*U_BU

Darstellung Schmutzwasserbeseitigung

- Schmutzwasserkanal *E*Z_BZ
- Mischwasserkanal *E*Z_BZ
- Abwasserdruckleitung *E*Z_BZ
- Vakuumleitung *E*Z_BZ
- schmutzwasser *E*U_BZ
- schmutzwasser *E*U_BU
- Schmutzwasser geplant

Darstellung Niederschlagswasserbeseitigung

- Regenwasserkanal *E*Z_BZ
- Regenwasserkanal *E*U_BZ
- Regenwasserkanal *E*U_BU
- Regenwasser geplant

Darstellung Gewässer

- Gewässer *E*U_BU

Darstellung Kabel

- Steuerkabel *E*Z_BZ
- Leistungskabel *E*Z_BZ
- Lichtwellenleiter *E*Z_BZ
- Kabel *E*U_BU

Darstellung Fernwärme

- Fernwärme
- Fernwärmevorlauf
- Fernwärmerücklauf

Darstellung technische Anlagen

- Abluft *E*Z_BZ
- Belebtschlamm *E*Z_BZ
- Brunnen *E*Z_BZ
- Druckluft *E*Z_BZ
- Enthärtungsfiltrat *E*Z_BZ
- Enthärtungskonzentrat *E*Z_BZ
- entwässerter Faulschlamm *E*Z_BZ
- Erdgas *E*Z_BZ
- Erdung *E*Z_BZ
- externe Schlämme *E*Z_BZ
- Fakalien *E*Z_BZ
- Fällmittel *E*Z_BZ
- Faulschlamm *E*Z_BZ
- Flockungsmittel *E*Z_BZ
- Klärgas *E*Z_BZ
- Klarwasserablauf *E*Z_BZ
- Luft (Abwasser) *E*Z_BZ
- Luft (Trinkwasser) *E*Z_BZ
- Notüberlauf *E*Z_BZ
- Primärschlamm *E*Z_BZ
- Rückkauftschlamm *E*Z_BZ
- Sauerstoff *E*Z_BZ
- Schlämme *E*Z_BZ
- Spülabwasser *E*Z_BZ
- Spülluft *E*Z_BZ
- Topografie *E*Z_BZ
- Trübwasser *E*Z_BZ
- Überschussschlamm *E*Z_BZ
- Überschussschlamm eingedickt *E*Z_BZ
- Wärme heiß *E*Z_BZ
- Wärme kalt *E*Z_BZ

Darstellung Schutzrohre

- Schutzrohr

lagerunsicher alle Leitungen — außer Betrieb alle Leitungen

stillgelegt alle Leitungen

Flurstück mit Flurstücknummer

Gebäude mit Hausnummer

*E : Eigentümer
**B : Betreiber
***Z : Ver. / Entsorgungsunternehmen (VEU)
****U : ungleich VEU

Hinweis! Mit Lage- und Höhenabweichungen des Leitungsbestandes muss gerechnet werden. Bei Arbeiten am Leitungsbestand sind deshalb geeignete Maßnahmen zu ergreifen, um Beschädigungen zu vermeiden.

Titel

Maßstab 1: 500

Datum: 18/02/2026

Lagebezug ETRS89 / UTM zone 33N

Höhenbezug DHHN2016

Nutzerkürzel: zvgjl

Blatt-Nr.: 1

Vorhabensbezeichnung

Vorhaben, möglichst ausführliche Angaben zum Anlass der erforderlichen Bestandsausgabe angeben!

Lageangaben

Lageangaben, möglichst Ort und Straße eintragen

Zweckverband Grevesmühlen
Wasserversorgung und Abwasserbeseitigung
- Körperschaft des öffentlichen Rechts -

© Zweckverband Wasserversorgung und Abwasserbeseitigung Grevesmühlen,
Karl-Marx-Str. 7/9,
23936 Grevesmühlen,
Telefon: 03881/7570,
info@zweckverband-gvm.de